



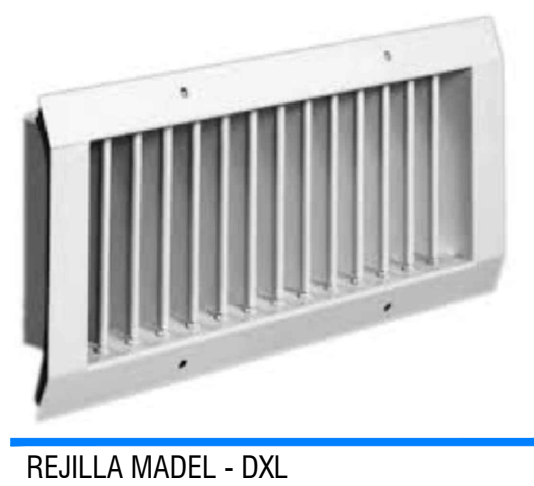

LEYENDA DE ACTUACIONES	
1	APERTURA HUECO Y COLOCACIÓN PUERTA CORTA FUEGOS EI ₄₅ -CS CON ELECTROMÁN
2	APERTURA HUECO Y COLOCACIÓN PUERTA
3	RECOLOCACIÓN PUERTA TRASTERO
4	ELIMINACIÓN DE TABIQUE
5	ELIMINACIÓN DE PUERTA
6	ELIMINACIÓN TRASTEROS PARA UBICAR ZONA DE DESCARGA
7	RESISTENCIA AL FUEGO DE LAS PAREDES QUE DELIMITAN EL SECTOR DE INCENDIO EI-120
— TABIQUE DE PLADUR EI-120	

Núm:	01	Plano: OBRAS DE ADECUACIÓN PARA EL CUMPLIMIENTO DE LA NORMATIVA.	
Escala:			
		Proyecto: Actividad permanente mayor de nave destinada a trasteros.	
		Situación: C/ 16 de Julio, nº 56. Polígono Son Castelló - 07009 - Palma.	
 DAVID TORGERS BOUVRIE Ingeniero Técnico Industrial categoría nº 1135 Teléfono: 871 223 870 Mail: dtorgers@qntm-management.com		Nº Expte: 25113 - INS	
		Nº: REVISION DE FECHA	
		01 CRR 17/12/2025	
		02 29/12/2025	
Titular:		03 XX-XX-XXXX	
		04 XX-XX-XXXX	

QNTM PROYECTOS Y MANEJO S.L.
C/ 16 de Julio, nº 56. Polígono Son Castelló - 07009 - Palma.
Teléfono: 677 223 670
Mail: dionisio@qntm-management.com

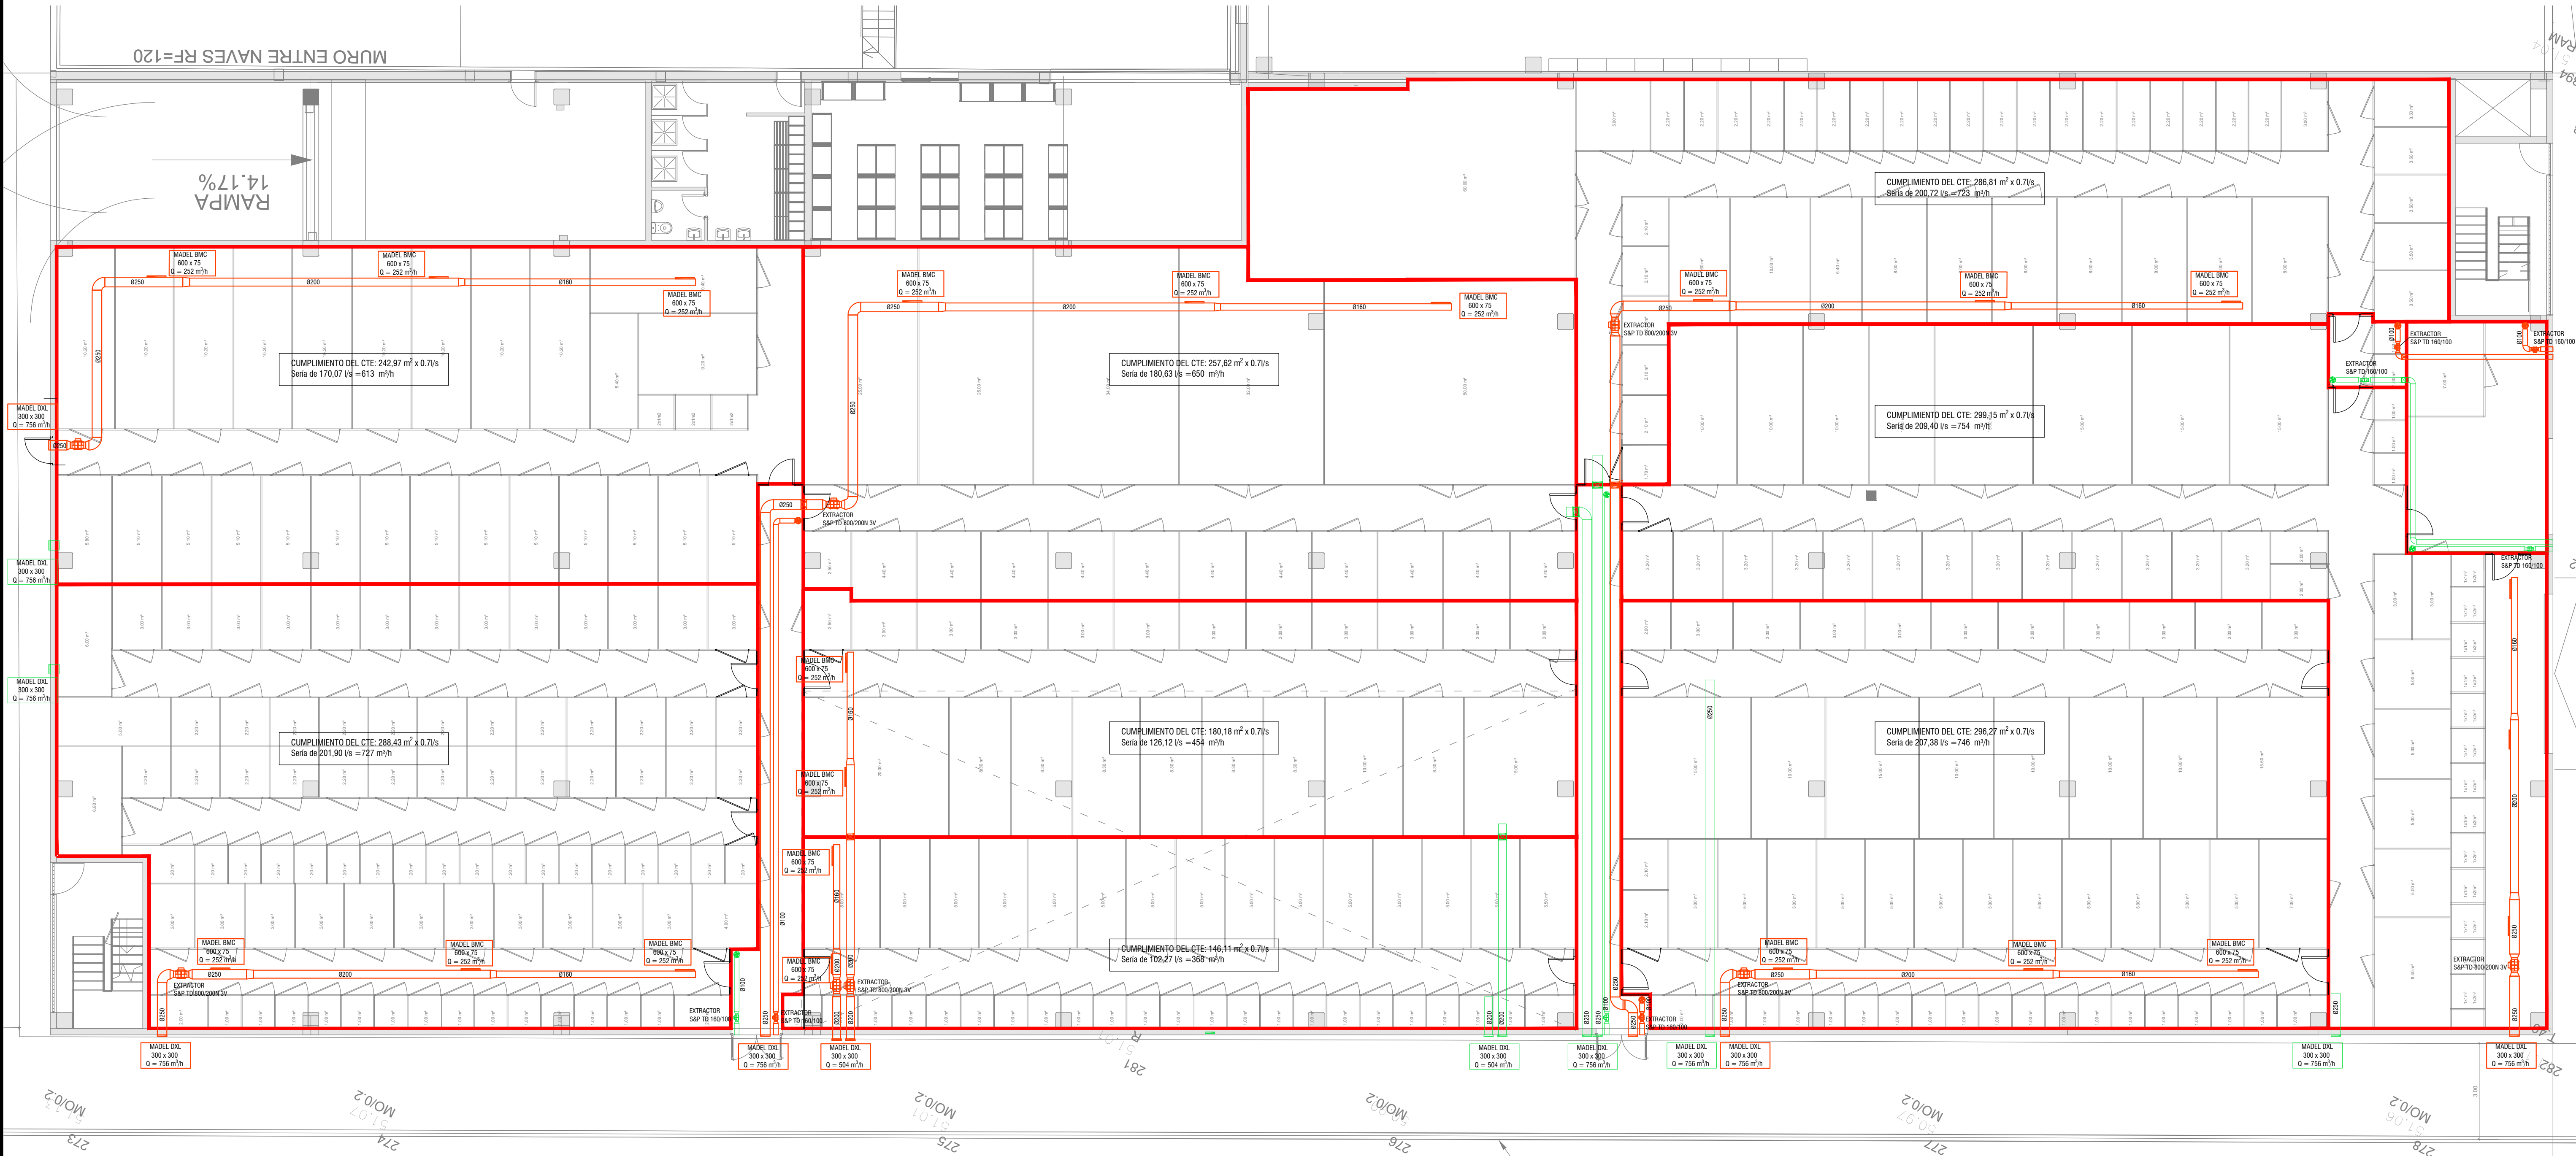

REJILLA MADELM - DXL



REJILLA MADELM - DXL

Tabla 2.2 Caudales de ventilación mínimos en Locales no habitables

Locales	Caudal mínimo q, en l/s	
	Por m² útil	En función de otros parámetros
Trasteros y sus zonas comunes	0.7	
Aparcamientos y garajes		120 por plaza
Almacenes de residuos	10	

CUMPLIMIENTO DEL CTE DB-HS3

LEYENDA DE VENTILACIÓN	
SÍMBOLO	DESCRIPCIÓN
	CONDUCTO CIRCULAR DE APORTACIÓN/EXTRACCIÓN
	REJILLA DE APORTACIÓN
	REJILLA DE EXTRACCIÓN
	CAJA FILTRANTE
	EXTRACTOR

Núm:

02

Escala:

1/100

QNTM

PROYECTOS Y MAQUETACIÓN

CIEN TIGERIS BOUVRE

Industria, Tecnología Industrial, Colaps nº 1135

Teléfono: 677 223 670

Mail: domini@qntm-management.com

Plano:

INSTALACIÓN DE VENTILACIÓN.

Proyecto:

Actividad permanente mayor de nave destinada a trasteros.

Situación:

C/ 16 de Julio, nº 56.
Polígono Son Castelló - 07009 - Palma.

Titular:

BOOKABOX SERVICE GMBH

Nº Expte:

25113 - INS

Nº:

REVISION DE

FECHA

01

CRR

17/12/2025

02


29/12/2025

03


XX-XX-XXXX

04



XX-XX-XXXX

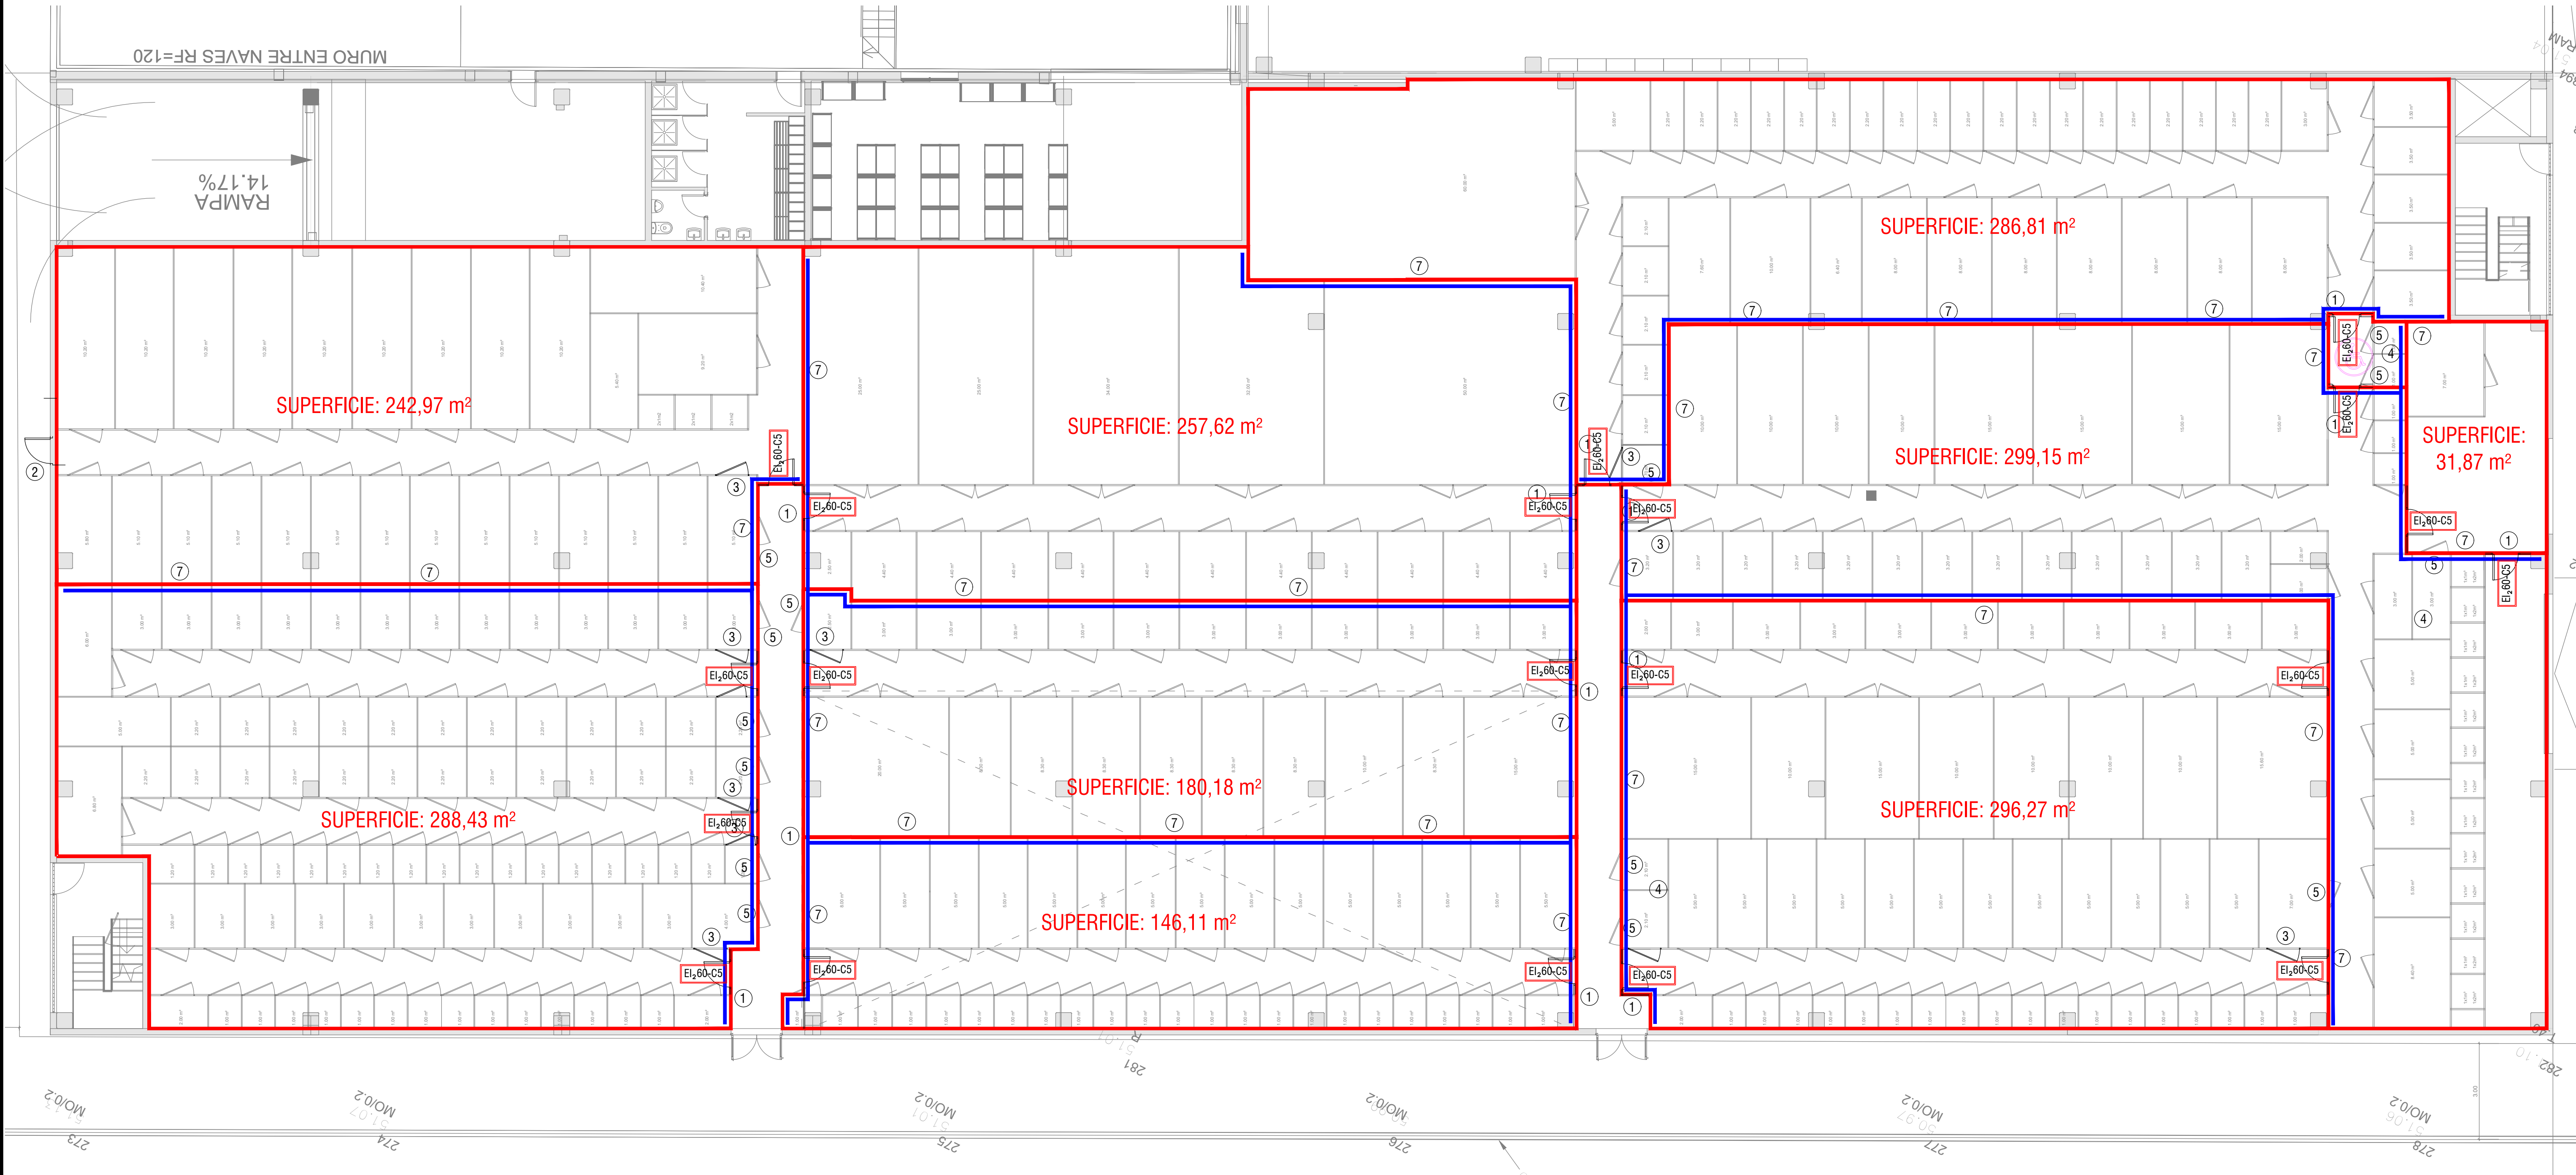

LEYENDA DE SECTORIZACIÓN	
	DELIMITACIÓN SECTOR
	TABIQUE DE PLADUR EI-120
	PUERTA CORTA FUEGOS EI, 60-C5

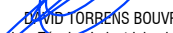Núm:	04	Plano:	
		SECTORIZACIÓN.	
Escala:		1/100	
QNTM PROJECTS & MANAGEMENT  CARLO TOBBERG BOUVRIE Ingénieur Thorwald Industrial college n° 1135 Téléphone: 471 223 870 Mail: dommes@qntm-management.com		Proyecto:	
		Actividad permanente mayor de nave destinada a trasteros.	
Situación: C/ 16 de Juliol, nº 56. Polígono Son Castelló - 07009 - Palma.		Nº Expte: 25113 - INS	
		Nº: REVISION DE FECHA	
		01 CRR 17/12/2025	
		02 29/12/2025	
		03 XX-XX-XXXX	
Titular: BOOKABOX SERVICE GMBH		04 XX-XX-XXXX	



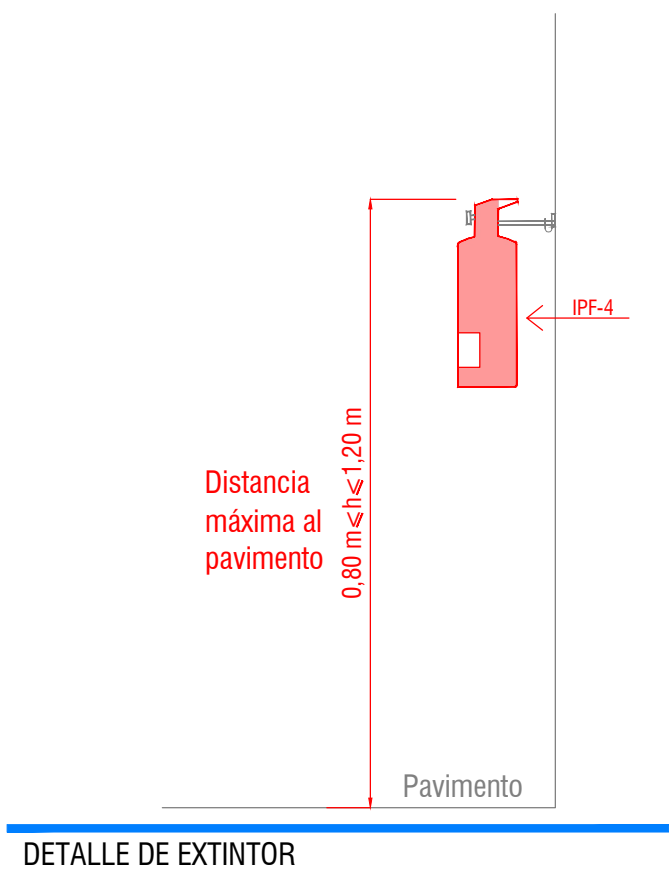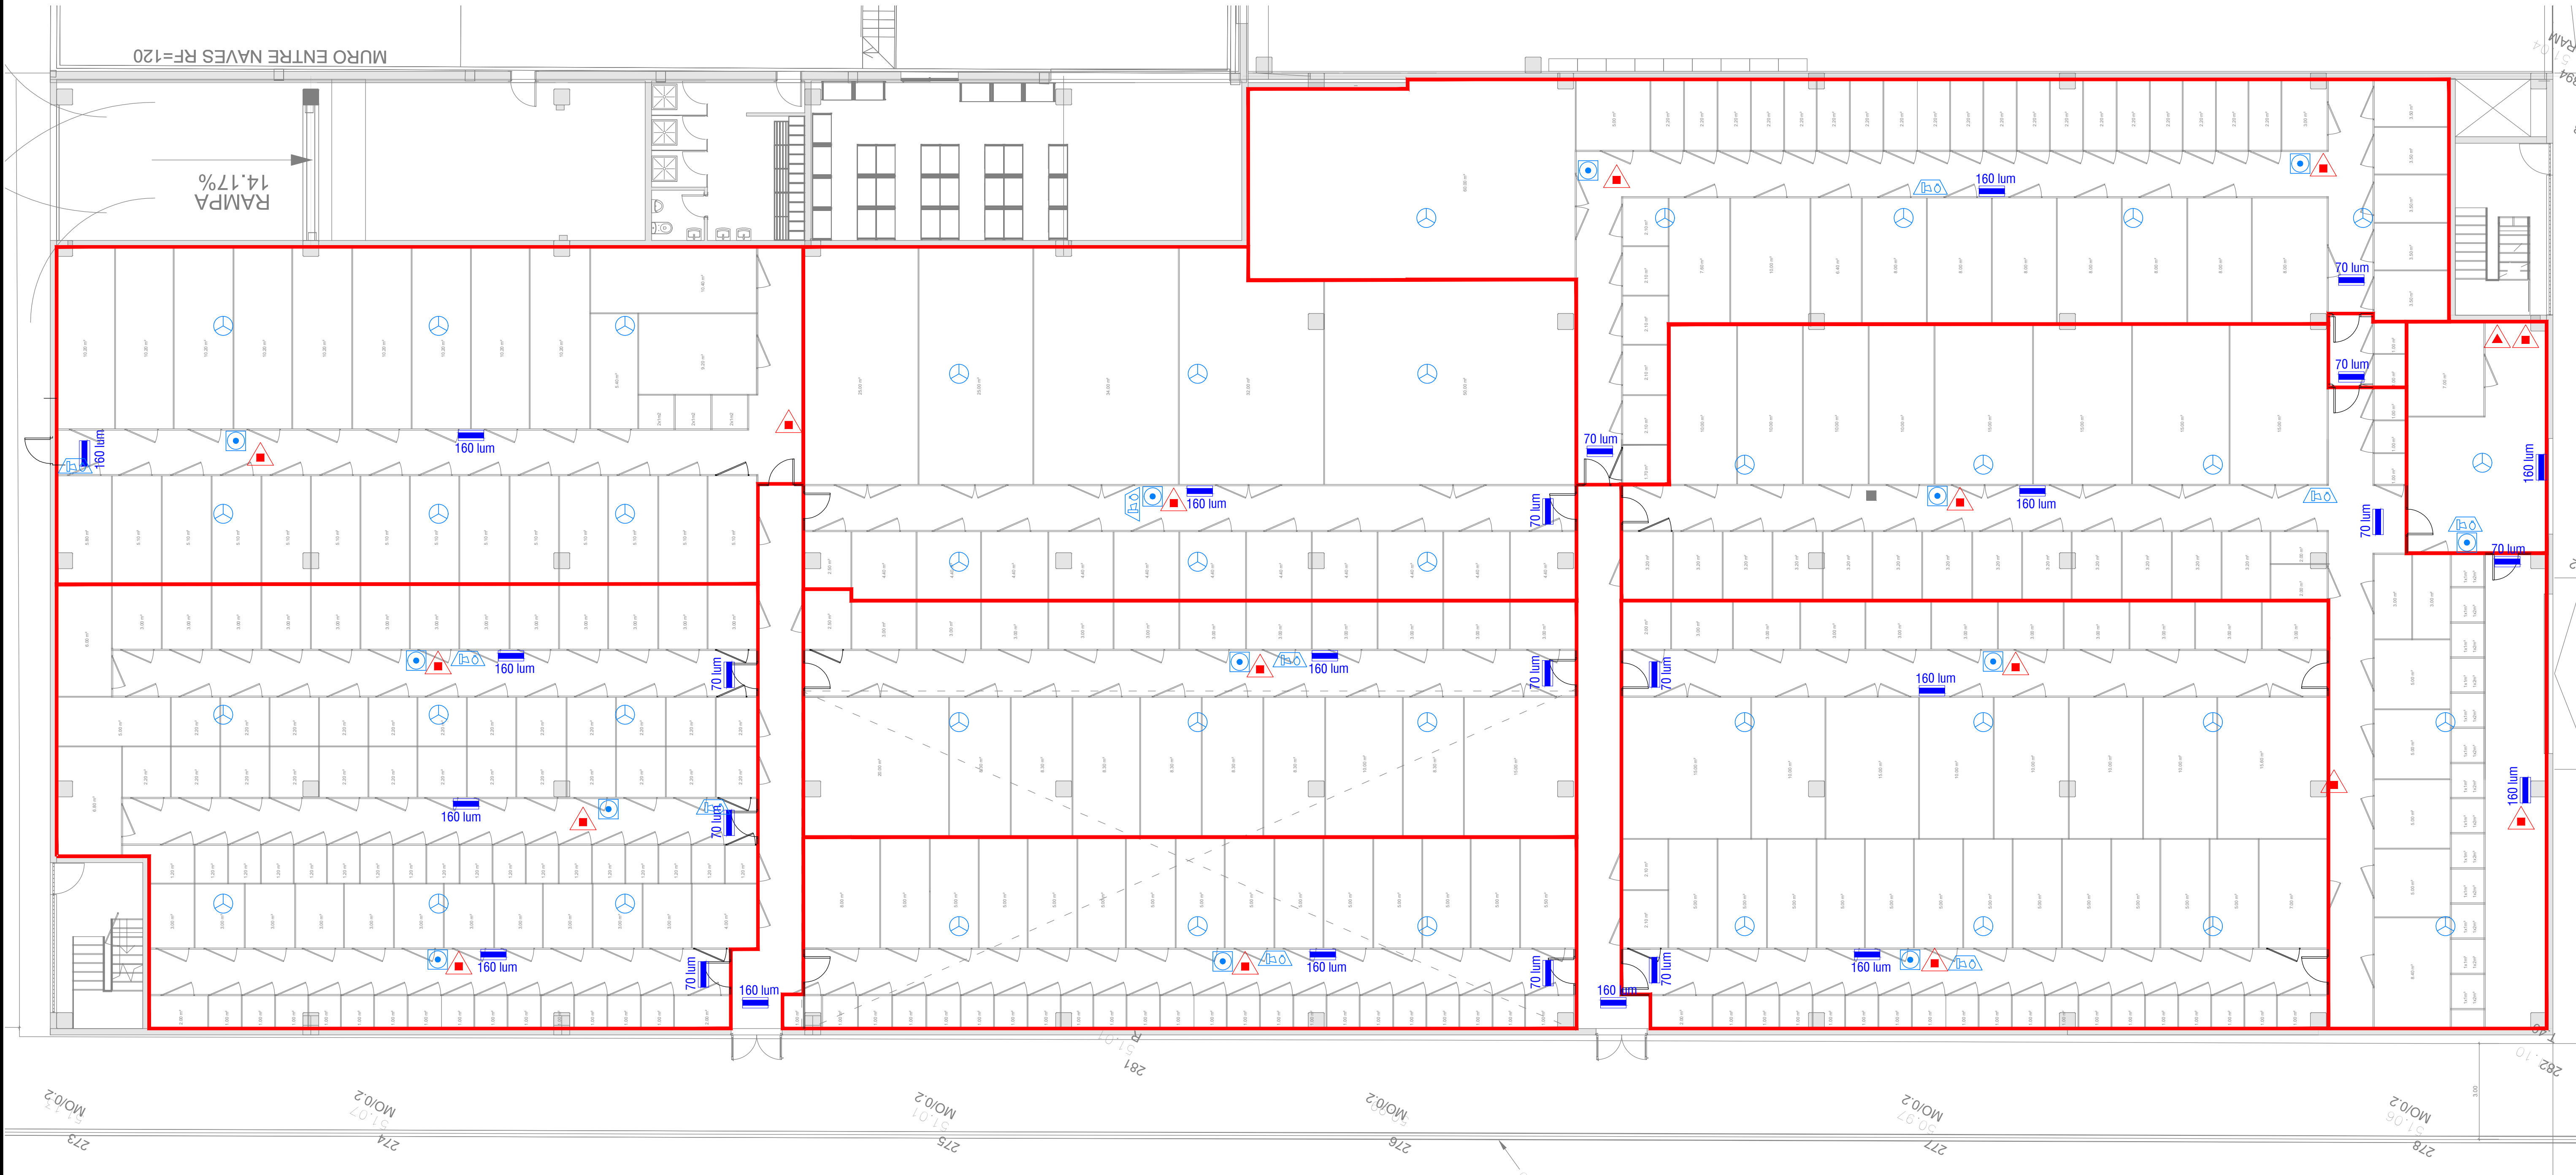

LEYENDA DE PROTECCIÓN CONTRA INCENDIOS	
	CUADRO ELÉCTRICO
	EXTINTOR POLVO SECO 21A-113B (6Kg)
	EXTINTOR CO2 (5Kg)
	LUMINARIA AUTÓNOMA DE EMERGENCIA
	PULSADOR MANUAL DE ALARMA
	BALIZA ÓPTICO-ACÚSTICA DE ALARMA CONTRA INCENDIOS
	DETECTOR ÓPTICO DE HUMOS

Núm:

04

Escala:

1/100

Proyecto:

Actividad permanente mayor de nave destinada a trasteros.

Situación:

C/ 16 de Julio, nº 56.
Polígono Son Castelló - 07009 - Palma.

Titular:

BOOKABOX SERVICE GMBH

Nº Expte:

25113 - INS

Nº:

REVISIÓN DE

FECHA

01

CRR

17/12/2025

02


29/12/2025

03

XX-XX-XXXX

04

XX-XX-XXXX

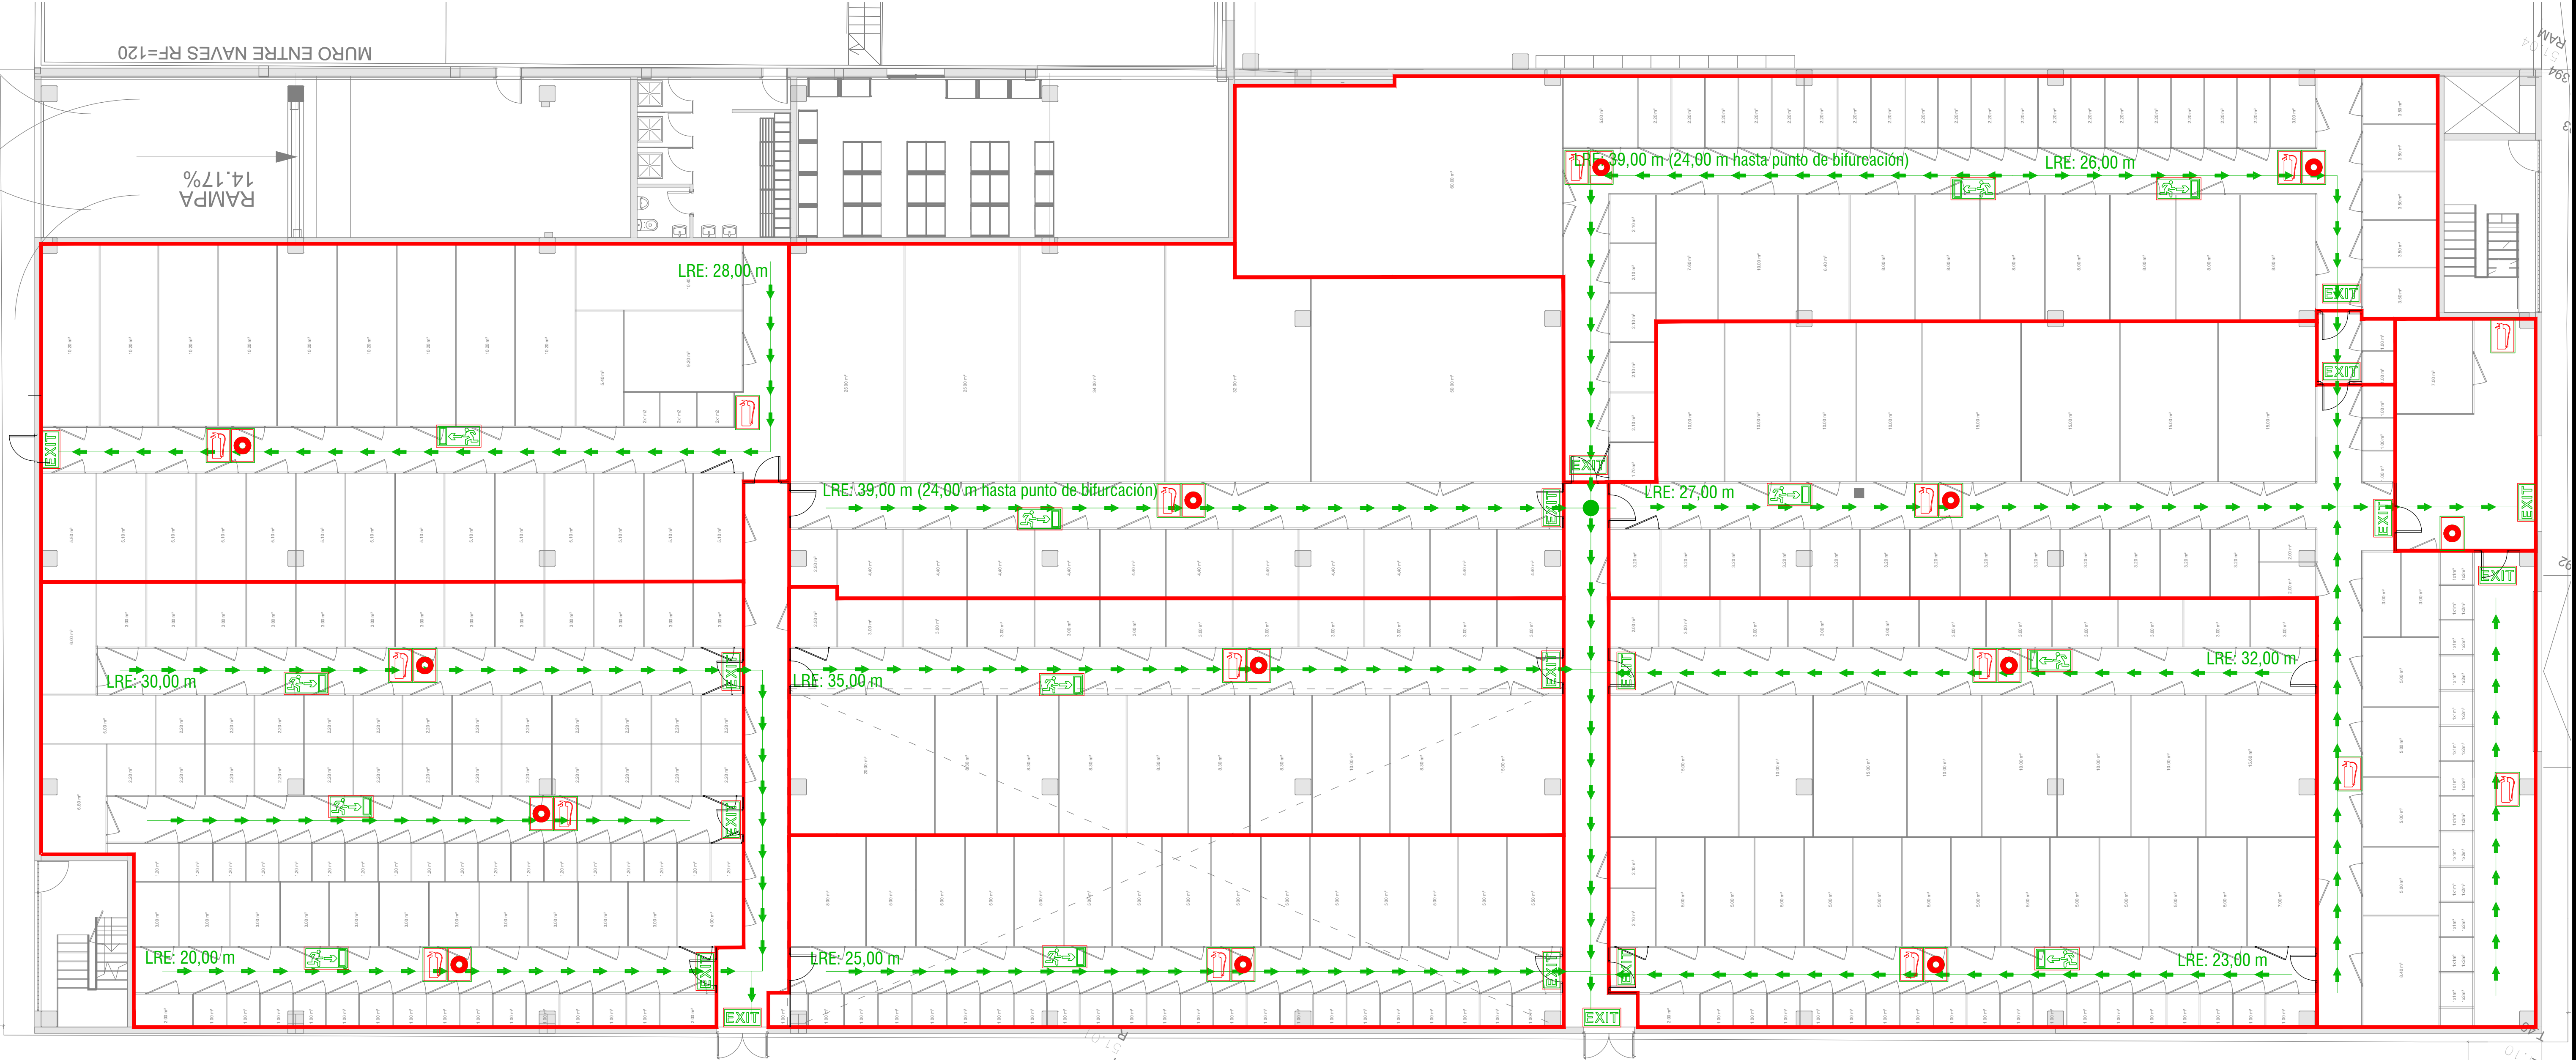

LEYENDA DE RECORRIDOS DE EVACUACIÓN	
	RECORRIDO DE EVACUACIÓN
LRE: XX m	LONGITUD MÁXIMA DE RECORRIDO DE EVACUACIÓN
	PUNTO DE BIFURCACIÓN

LEYENDA DE SEÑALIZACIÓN	
	SEÑAL FOTOLUMINISCENTE DE "SALIDA"
	SEÑAL FOTOLUMINISCENTE "SENTIDO DE EVACUACIÓN"
	SEÑAL FOTOLUMINISCENTE DE "EXTINTOR"
	SEÑAL FOTOLUMINISCENTE DE "PULSADOR"

Núm: 05 Escala: 1/100	Plano: SEÑALIZACIÓN Y RECORRIDOS DE EVACUACIÓN.			
	Proyecto: Actividad permanente mayor de nave destinada a trasteros.			
 QNTM PROJECTS & MANAGEMENT D.ª ROSA TORRES BOURVE Ingeniero Técnico Industrial categoría nº 1135 Teléfono: 677 223 670 Mail: dtorres@qntm-management.com	Situación:	Nº Expte: 25113 - INS		
	C/ 16 de Julio, nº 56. Polígono Son Castelló - 07009 - Palma.	Nº:	REVISIÓN DE FECHA	
	Titular: BOOKABOX SERVICE GMBH	01	17/12/2025	
		02	29/12/2025	
		03	XX-XX-XXXX	
04		XX-XX-XXXX		